© 120516528/10278

Wortmann Massivholztreppen GmbH
Blintroper Weg 7
58802 Balve-Garbeck
Telefon : 02375 - 205492-0
Fax : 02375 - 205492-30

Außendienst : JW
Aufmaß von : JW
gez. von : CW 17.04.18

Datenblatt für Projekt Nr. : 18-063


Auftraggeber

Sabrina und Stephan Sladek
Hinterm Garten 6
58708 Menden
Telefon : 0176/24926081
Fax : 02372/557773 (Herr Sladek Arbeit)
eMail :

Bauvorhaben :
Anlage / Etage :
Treppenname : Sladek
Komission / Bvh. : Sladek
Ansprechpartner :
Telefon / Handy : 0176/24926081

Montage durch: *Fa. Wortmann*
Baustellen-adresse :

Geländertragende Treppe mit waagerechten Wandbolzen

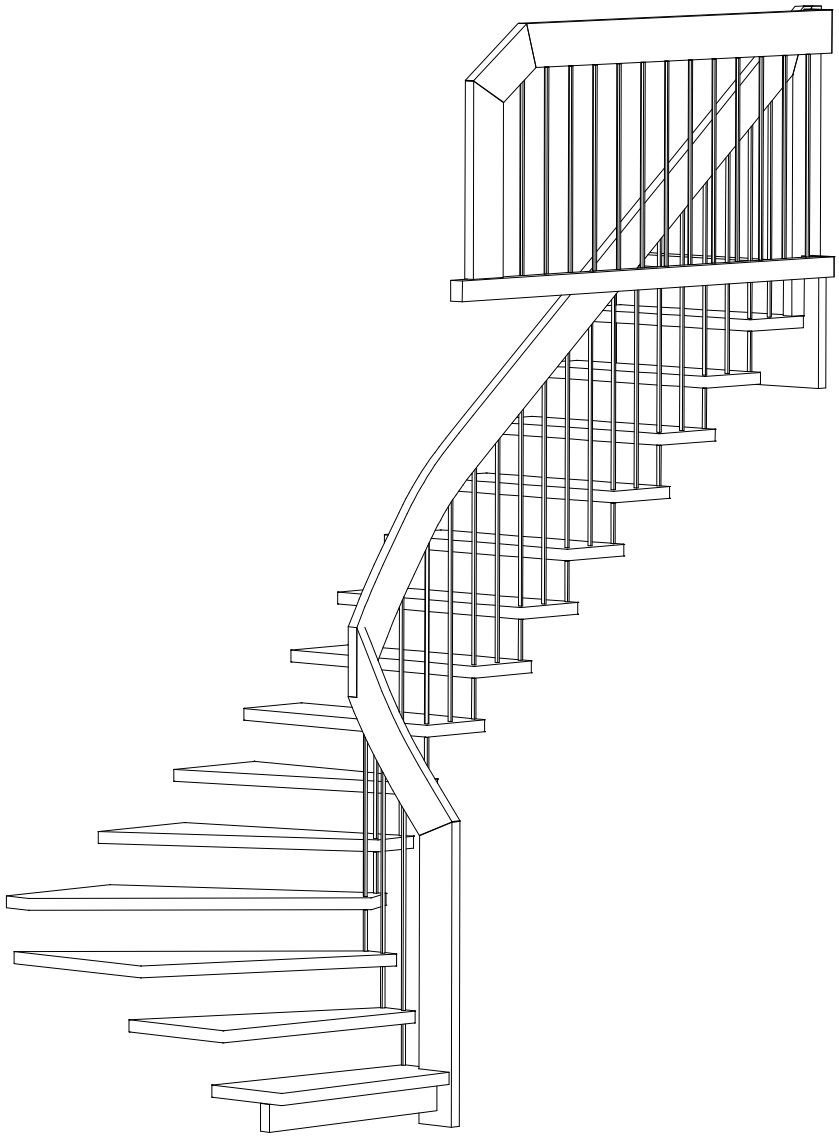

Materialstärke und Ausführung

Wangenst. außen	19.0 mm
Wangenst. innen	
Handlaufstärke	44.0 mm
Stufenstärke	44.0 mm
Setzstufenstärke	0.0 mm
Pfosten Ant. :	
Pfosten Eck. :	
Pfosten Aust. :	
Handlauf Typ :	HL2 44/160 (OK r=5mm

Geländerstäbe :

Innen :	E 16 - beidseitig M10
Außen :	
Material :	Edelstahl rund 16 mm
Oberfl.:	

Material und Oberfläche

Wangen Eiche keilgezinkt A/B
Oberfl.: *geölt*

Handlauf Eiche keilgezinkt A/B
Oberfl.: *geölt*


Stufen Eiche keilgezinkt A/B
Oberfl.: *geölt*

Setzstufen
Oberfl.:

Pfosten Eiche keilgezinkt A/B
Oberfl.: *geölt*

Deckenloch unter dieser Treppe : **Nein**

Genaue Vermassung der Treppe siehe Treppenzeichnung (Draufsicht)

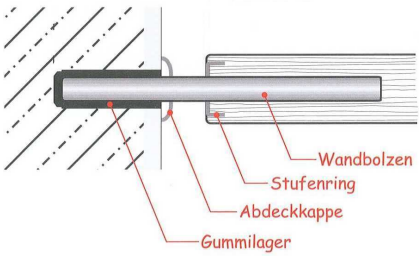

Verbindung der Trittstufe zur Wand hin mit waagerechten Tragbolzen in Gummilager.

Diese Zeichnung entspricht in der Ausführung meinen Bestelldaten, mit meiner Unterschrift erteile ich als Auftraggeber die Freigabe zur Produktion :

Datum und Unterschrift


© 120516528/10278

WORTMANN Massivholztreppen

Wortmann Massivholztreppen GmbH
Blintroper Weg 7
58802 Balve-Garbeck
Tel. 02375 - 205492-0
Fax 02375 - 205492-30

Ansichten in 3D


Auftrag Nr. :	18-063	Erstellt von :	CW
Bauvorhaben :		Außendienst :	JW
Anlage :		Gedruckt am :	17.04.18
Treppe :	Sladek	Zeit :	14:24

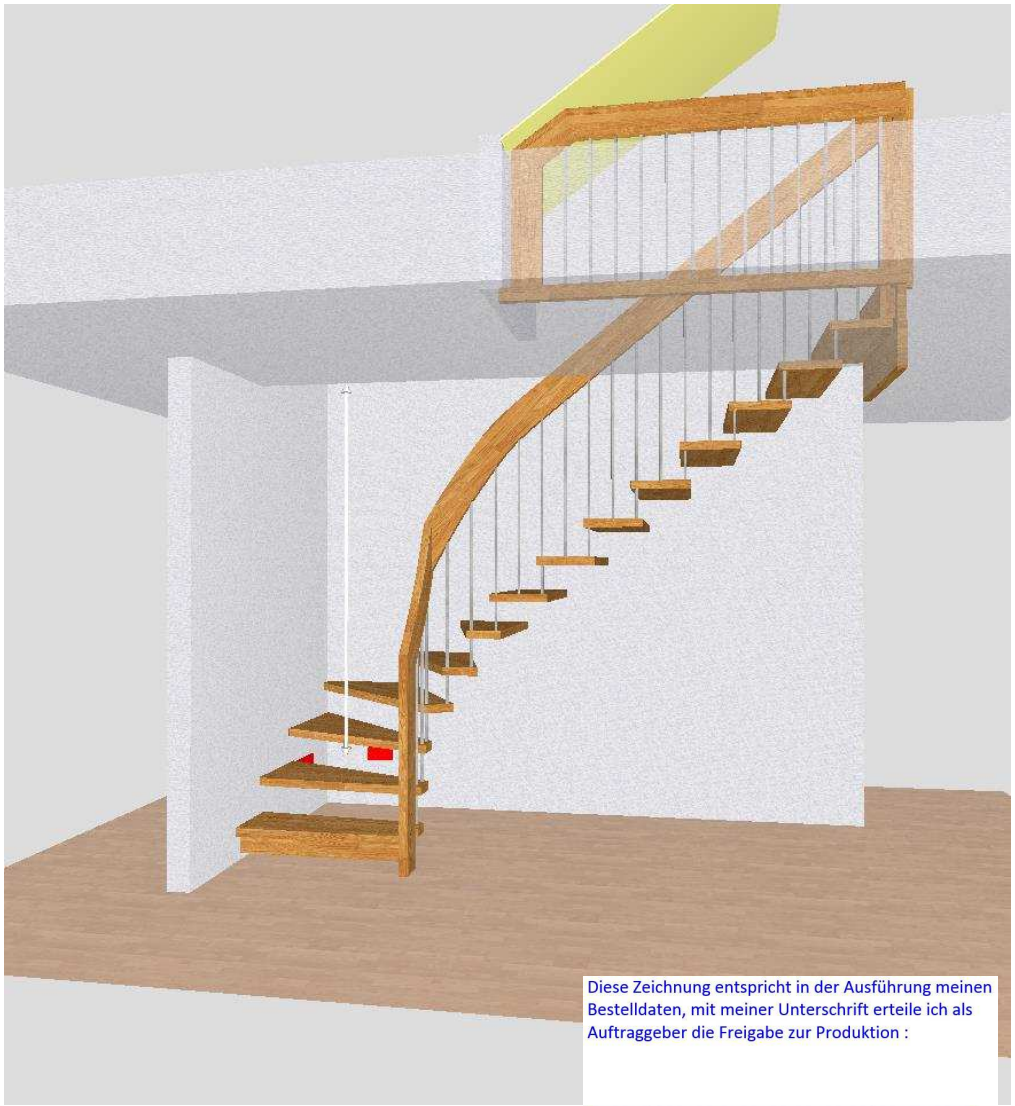


Diese Zeichnung entspricht in der Ausführung meinen Bestelldaten, mit meiner Unterschrift erteile ich als Auftraggeber die Freigabe zur Produktion :

Datum und Unterschrift



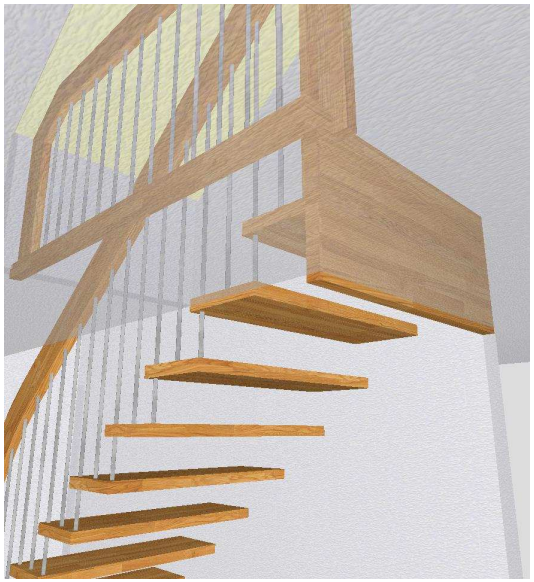

© 120516528/10278

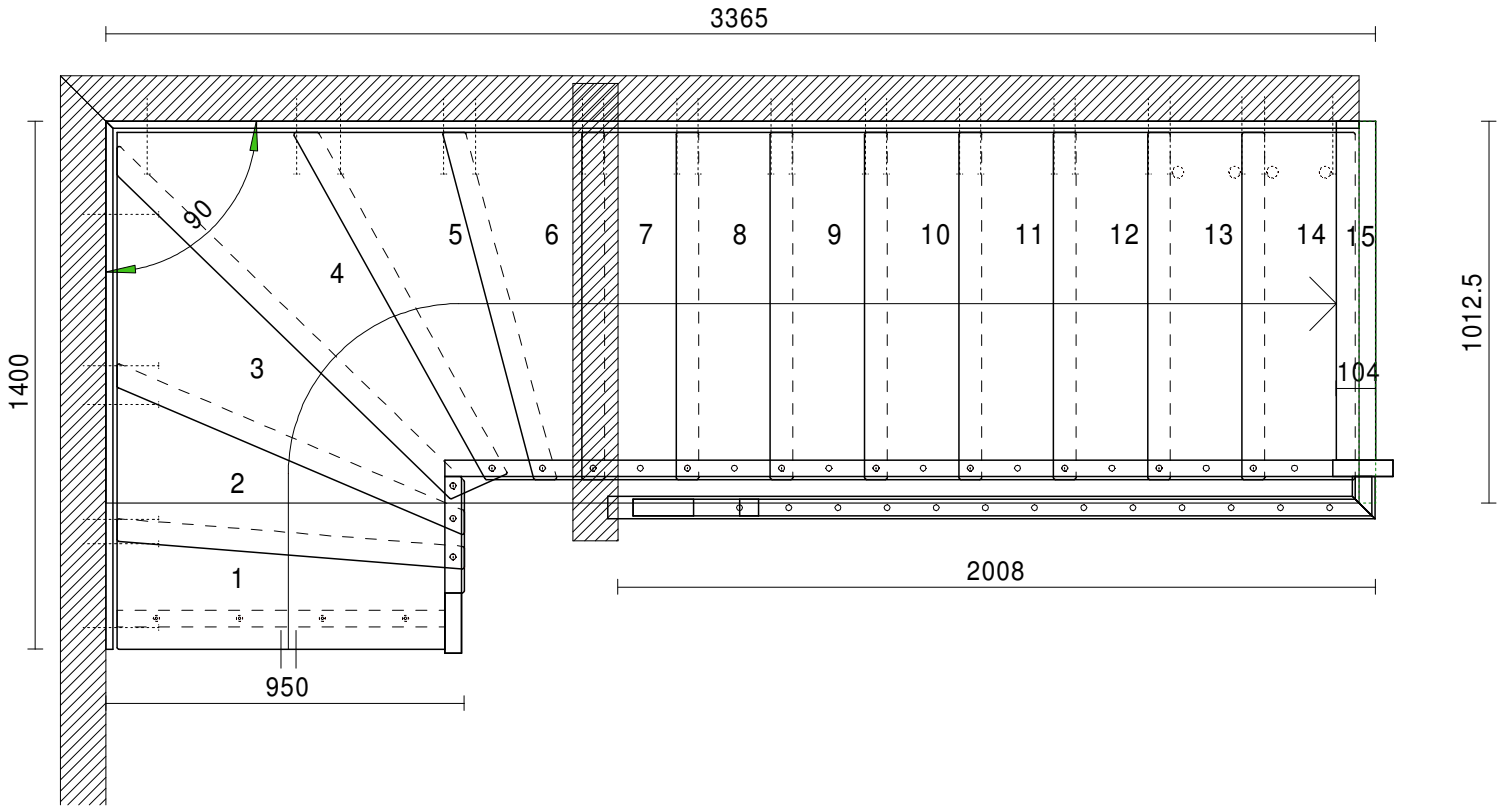

Geschoßhöhe : (OKFF - OKFF)	**2971.0 mm**
Belag oben :	50.0 mm
Belag unten :	0.0 mm
Deckenstärke :	446.0 mm insg.
Kopfhöhe :	2019.9 mm
Steigung:	198.1 mm
Auftrittsbreite :	250.0 mm
Schrittmaß :	646.1 mm
Neigungswinkel :	38.39 °
Stufenstärke :	44.0 mm
Wangen innen :	
Wangen außen :	19.0 mm
Pfosten Antritt :	44.0 mm*160.0 mm
Pfo. Wendelung :	
Pfosten Austritt :	44.0 mm*160.0 mm

Wangen : Eiche keilgezinkt A/B
geölt

Stufen : Eiche keilgezinkt A/B
geölt

Setzstufen :

Pfosten : Eiche keilgezinkt A/B
geölt

Handläufe : Eiche keilgezinkt A/B
HL2 44/160 (GK r=5mm)

Stab innen : E 16 - beidseitig M10

Stab außen :

Diese Zeichnung wurde auf Maße und Ausführung geprüft, Fertigungsfreigabe erteilt:

Datum / Unterschrift

Kunde:	Sabrina und Stephan Sladek
Straße :	Hinterm Garten 6
PLZ / Ort :	58708 Menden
Telefonnr.:	0176/24926081
Faxnr.:	02372/557773 (Herr Sladek Arbeit)

W o r t m a n n
Massivholztreppen GmbH
Blintroper Weg 7
58802 Balve Garbeck
Telefon: 02375-205492-0
Telefax: 02375-205492-30
E-Mail: info@wotre.de

Auftrag :	**18-063**	**Anlage :**		**Maßstab**	17.04.18 14:24 Uhr
Bauvorhaben :	**Sladek**	**Treppe :**	**Sladek**	**1 : 20.00**	gez. von : CW